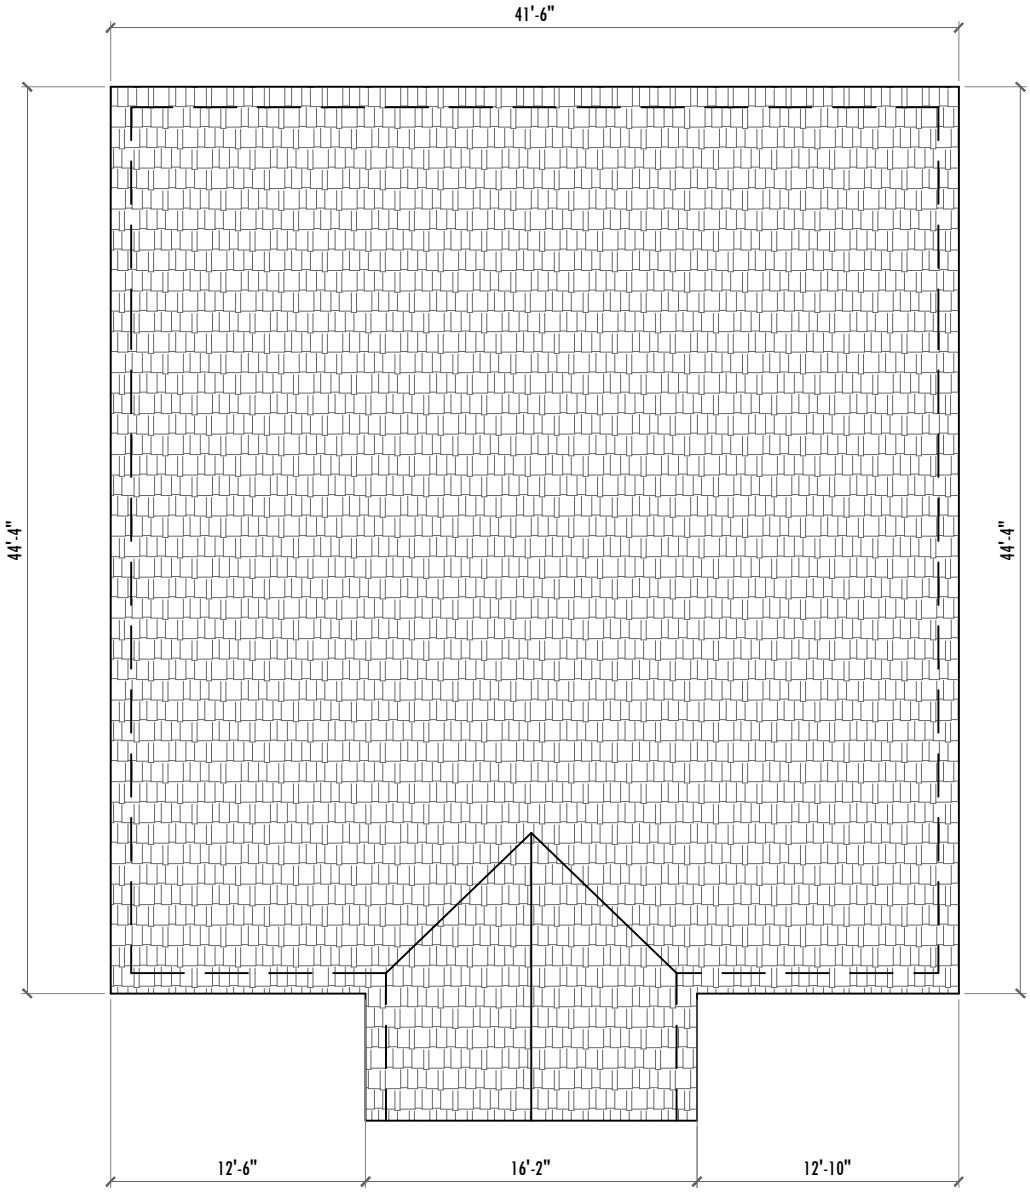

1
A-204

ROOF PLAN

SCALE: 1:50 MTS.

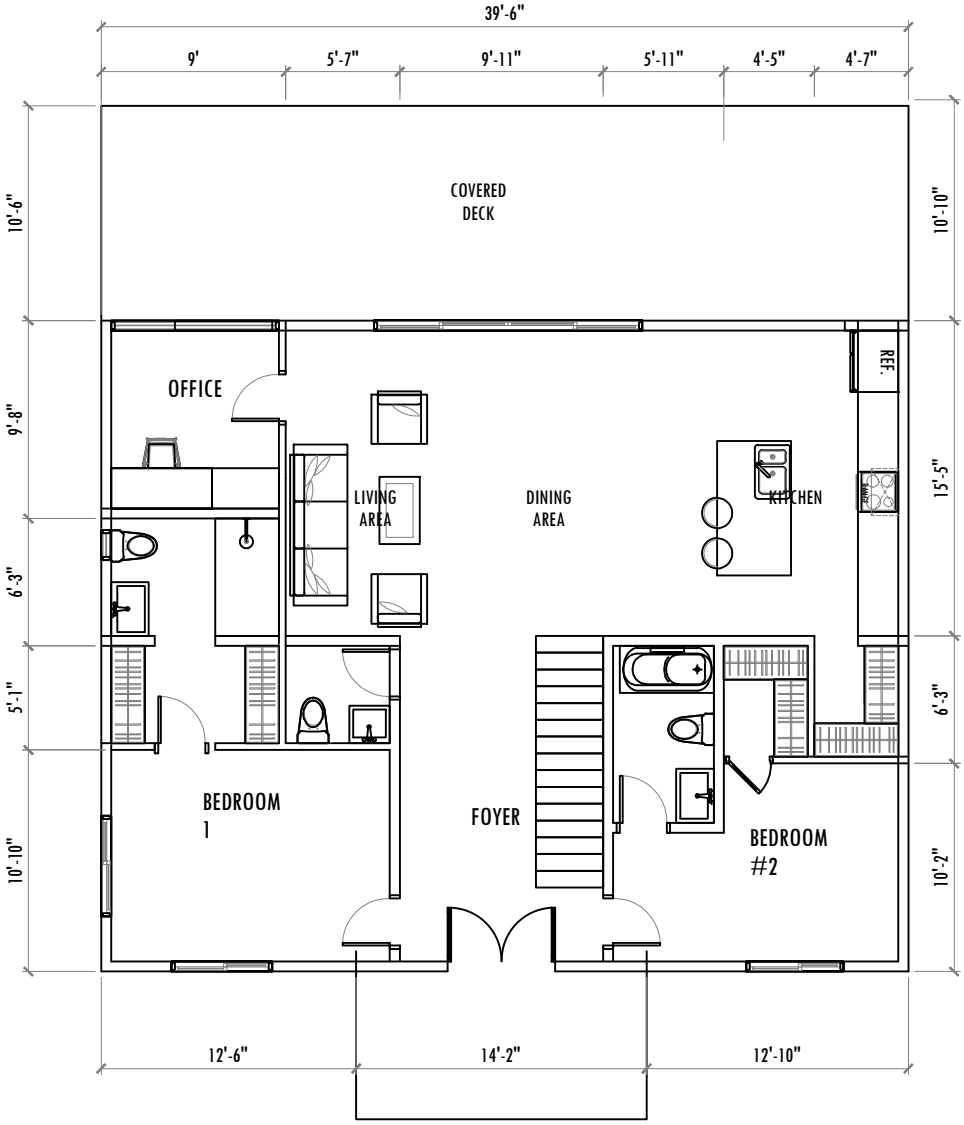

1
A-204

GROUND FLOOR PLAN

SCALE: 1:50 MTS.

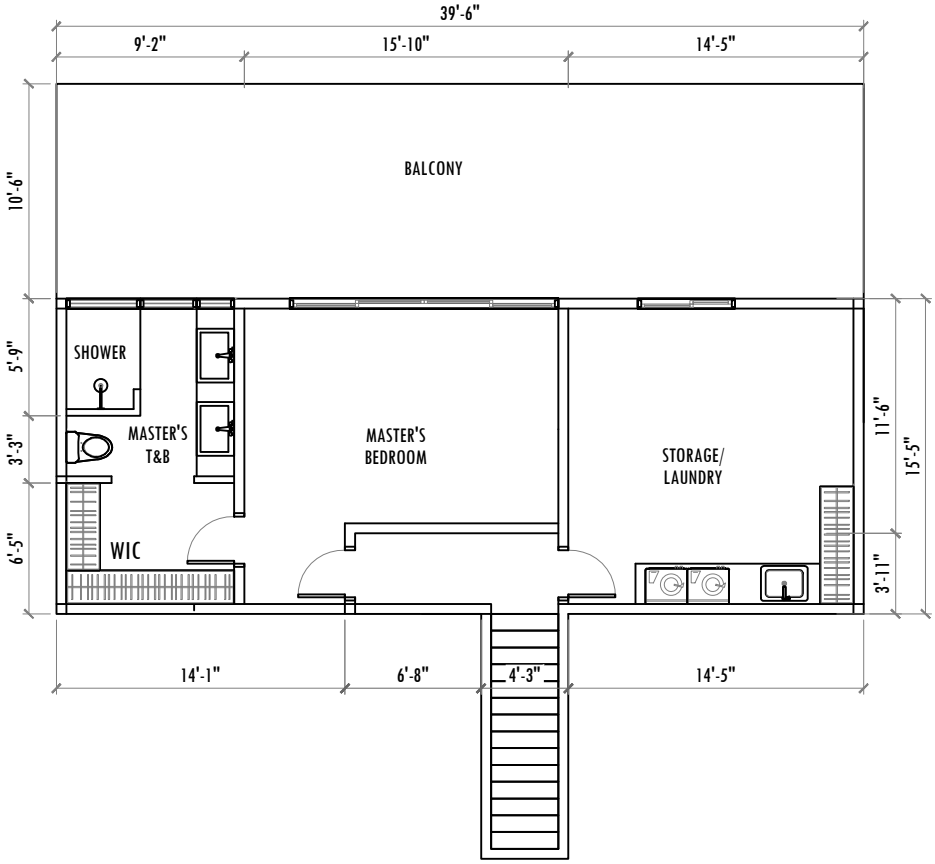

1
A-204

LOWER GROUND FLOOR PLAN

SCALE: 1:50 MTS.

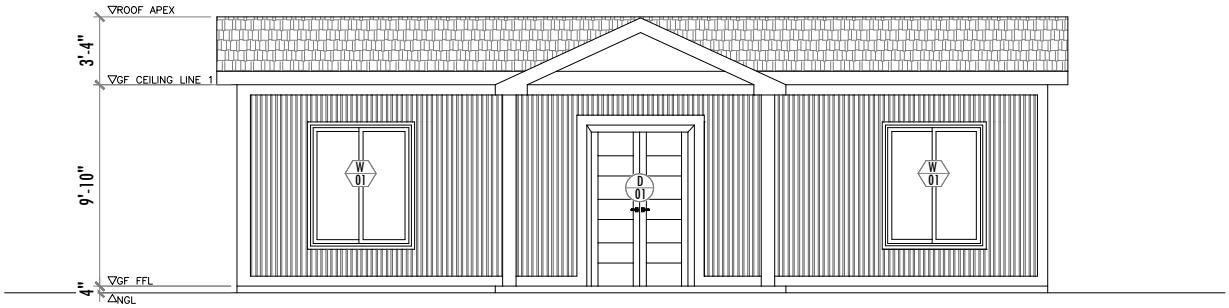

1
A-204
FRONT ELEVATION
SCALE: 1:50 MTS.

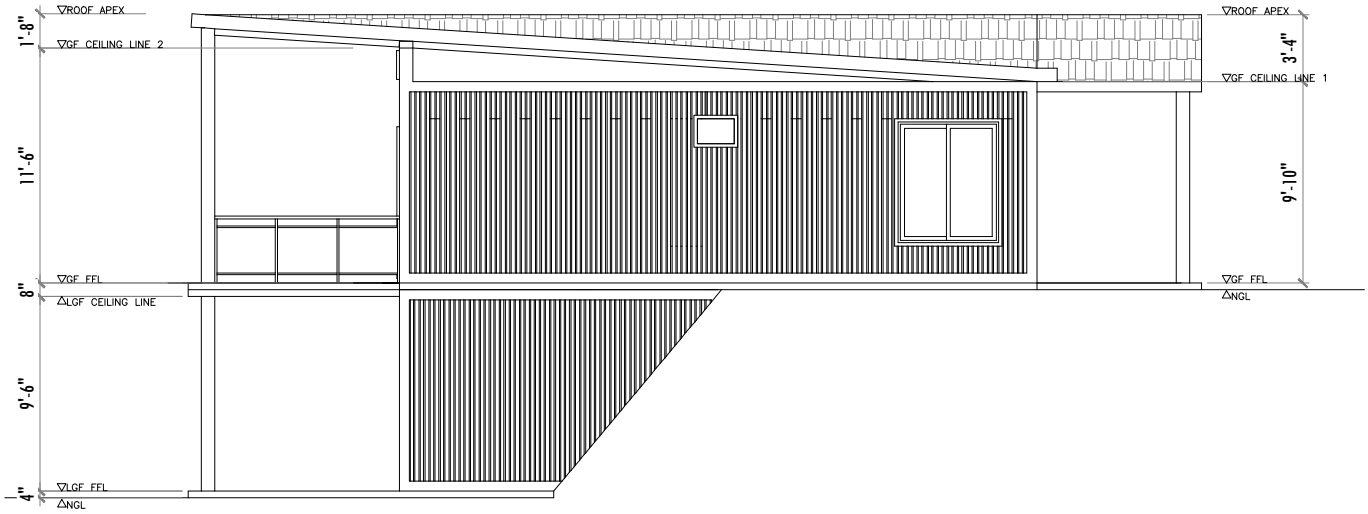

1
A-204
LEFT SIDE ELEVATION
SCALE: 1:50 MTS.

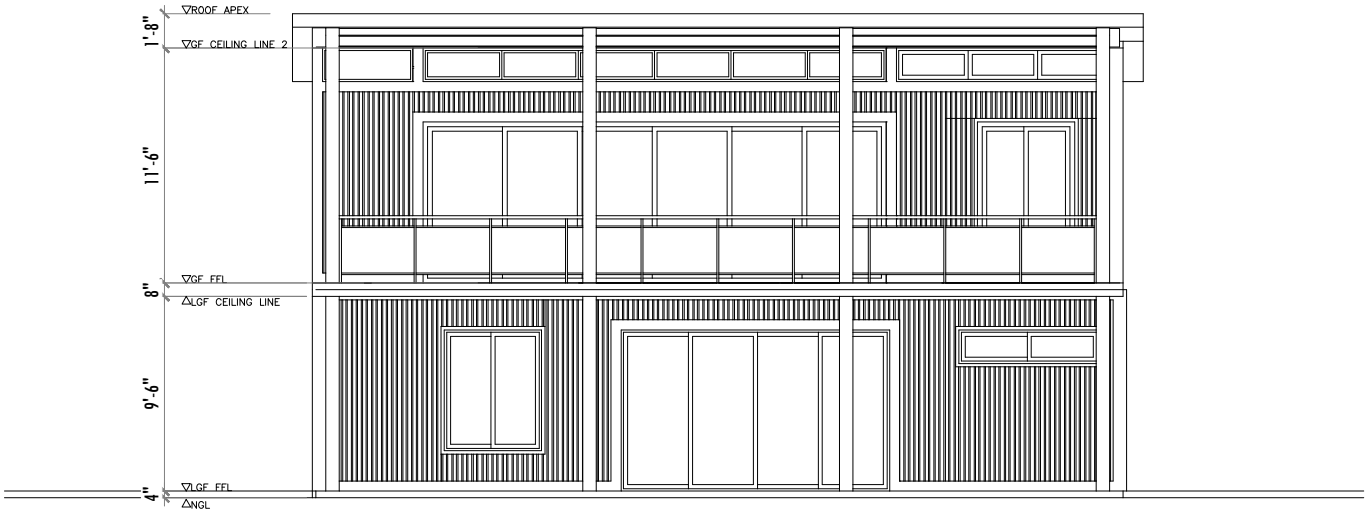

1
A-204

REAR ELEVATION

SCALE: 1:50 MTS.

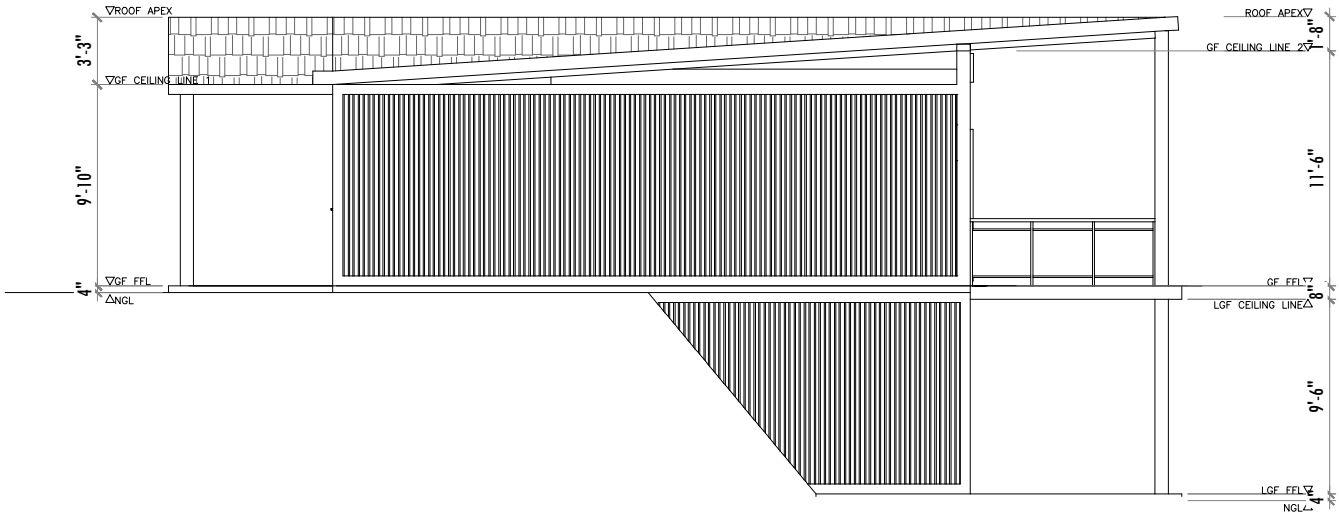

1
A-204

RIGHT SIDE ELEVATION

SCALE: 1:50 MTS.

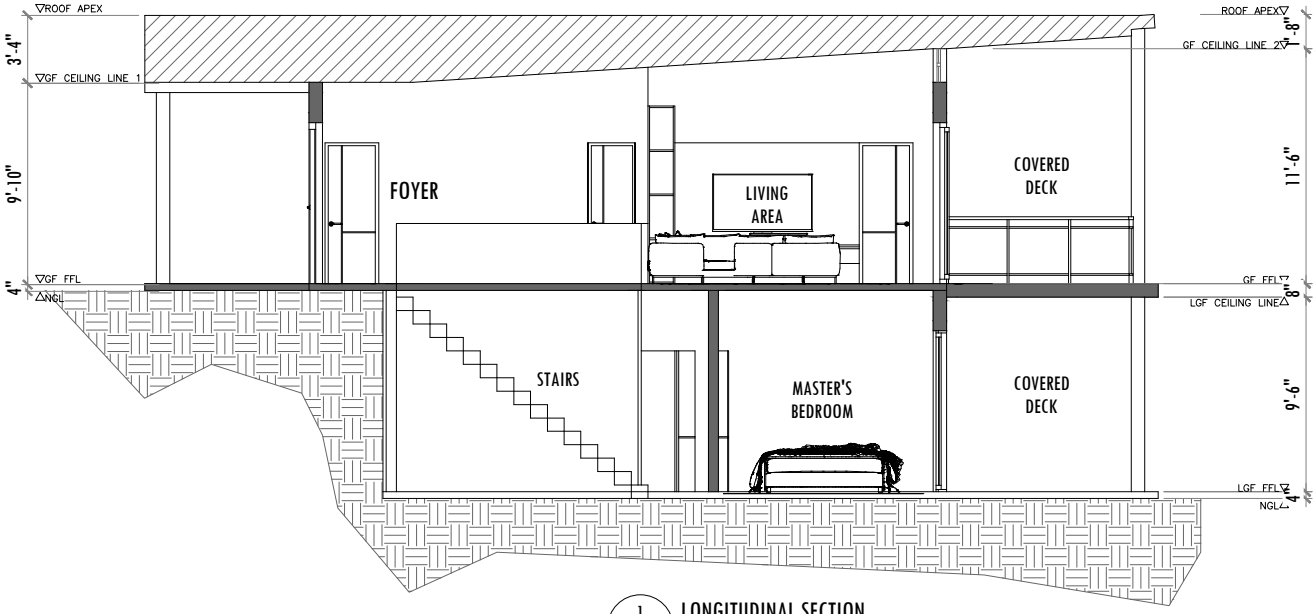

1
A-204
LONGITUDINAL SECTION
SCALE: 1:50 MTS.

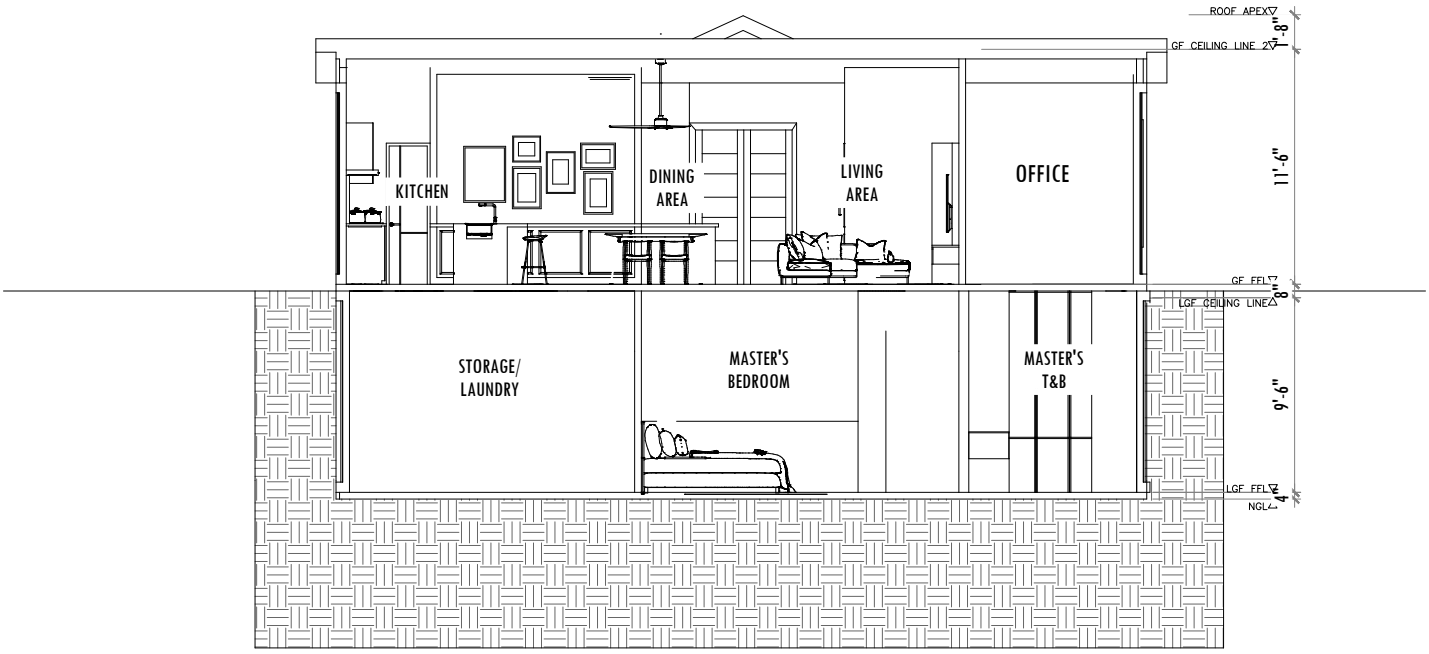

1
A-204
CROSS SECTION
SCALE: 1:50 MTS.